
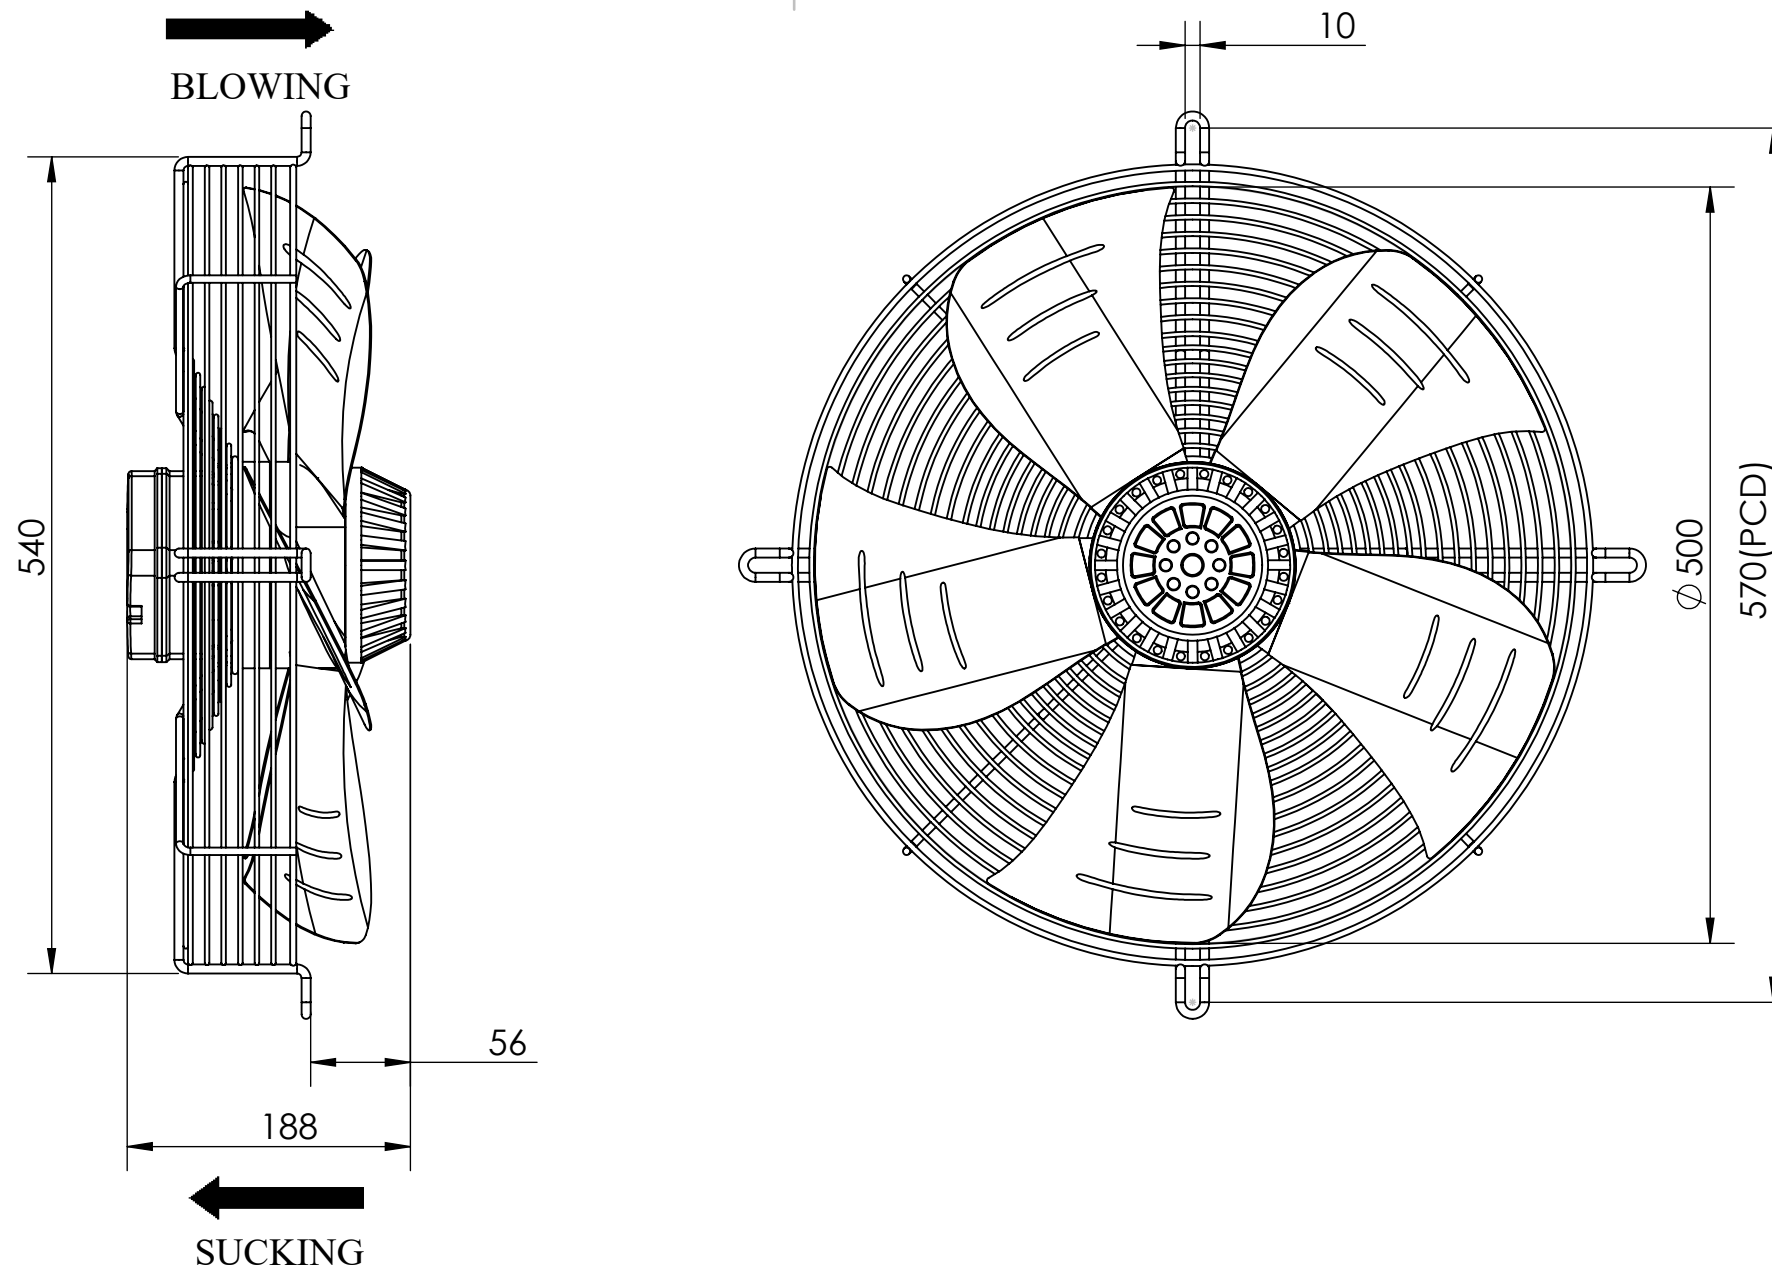


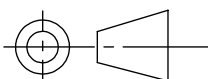

TECHNICAL SPECIFICATION:

TYPE	I/P SUPPLY	AMPS (A)	WATTS (W)	RPM	AIRFLOW		STATIC-PR (mm-WC)	dBA	CAP. μf	ADMISSIBLE AMBIENT TEMP	WEIGHT (Kg)
					CMH	CFM					
20 AF 3B4	415V,3Φ,50Hz	0.85	420	1350	6800	4000	13	70	..	60	9.5

- NOTE :
- ALL DIMENSIONS ARE IN mm.
 - INSULATION CLASS CLASS "F".
 - INGRESS PROTECTION RATING "IP-54".

UNLESS OTHERWISE SPECIFIED: DIMENSIONS ARE IN MILLIMETERS	THIRD ANGLE PROJECTION		4				 SUPERIOR ELECTRIC MACHINES PVT LTD B-214, 5th MAIN, PEENYA 2nd STAGE BANGALORE-58; Ph: 080 28361383,1742, 41171243 www.superiorelectric.in , info@superiorelectric.in "AN ISO 9001-2015 CERTIFIED COMPANY"
			3				
			2				
			1				
			SI NO	REVISION	DATE	SIGN	
DESIGNATION	NAME	SIGNATURE	DATE		TITLE:		
DESIGNED BY	SHRISHAILA		30-06-2026		20 AF 3B4-BG		
CHECKED BY	ABHILASH		30-06-2026				
APPROVED BY	GK		30-06-2026				
WEIGHT:		SCALE:1:10		SHEET 1 OF 1		DON'T SCALE THE DRAWING	

DWG NO.	MATERIAL:	A4
3006		